



T & L ENGENHARIA

ESTUDO DE VIABILIDADE


Estudo 1 - 2Q e 3Q, CA básico (2,5)

R. Alexandre Wisocki, 249 - Fazenda Velha - Araucária/PR


DIAGRAMA

- Rooftop – salão de festas/gourmet + terraço
- Pav. tipo 6x – 3x 2Q+3Q, 3x 2Q c/ suíte
- Térreo – pilotis / hall / estacionamento / lazer
- Subsolo – 36 vagas (não representado)

Altura estimada H = 23,28 m (térreo 3,00 + 6 x 2,88 + ático 3,00) • afastamento H/8 = 2,91 m

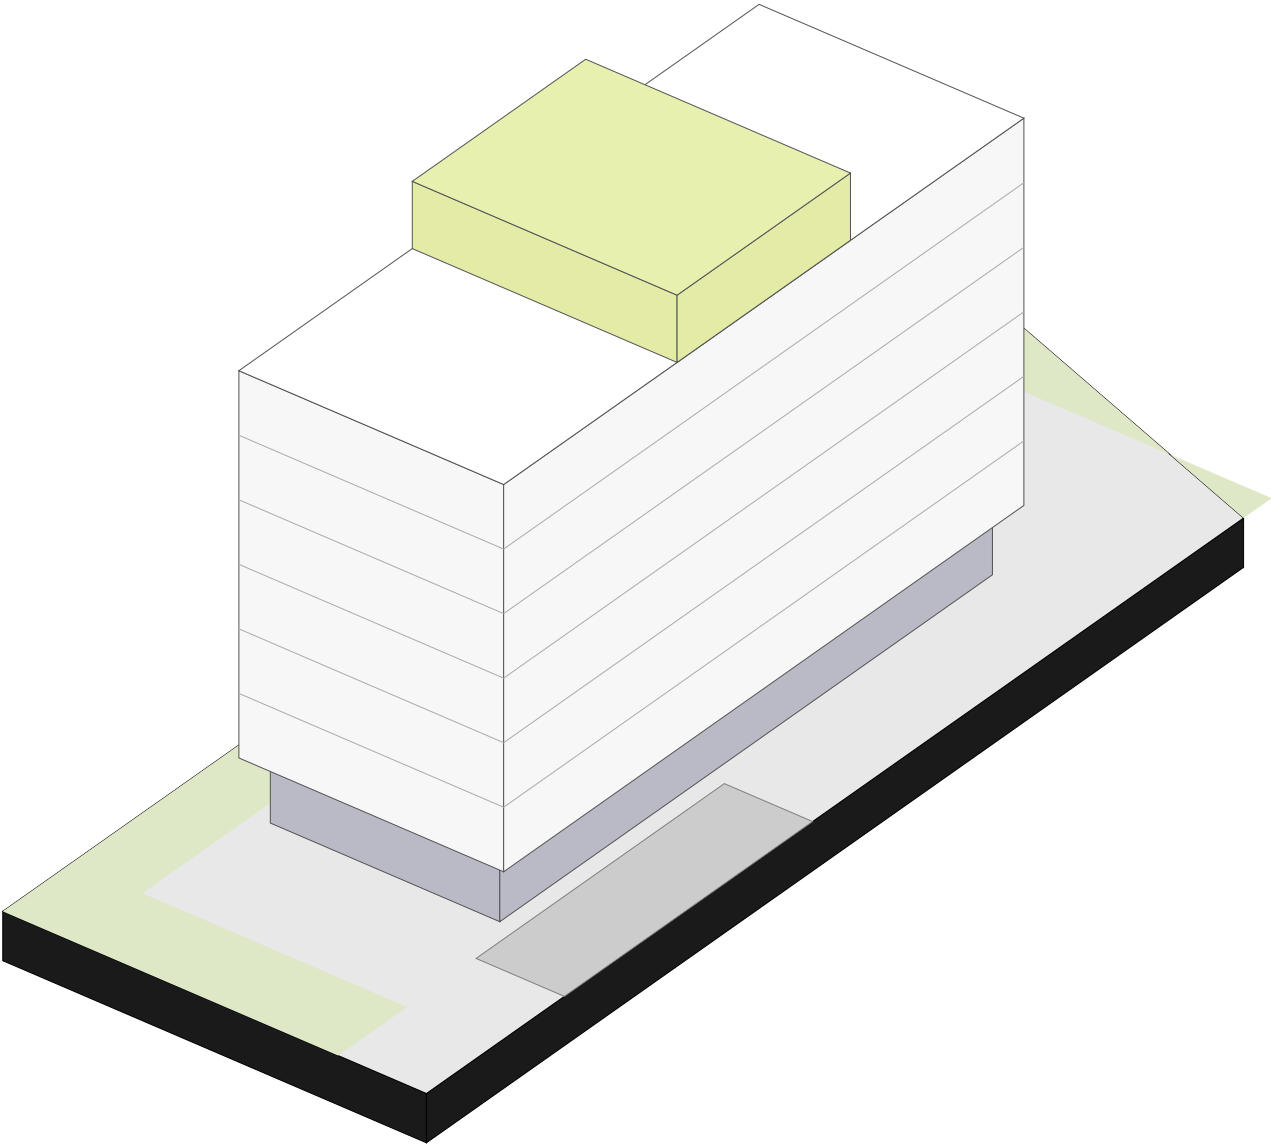

Diagrama

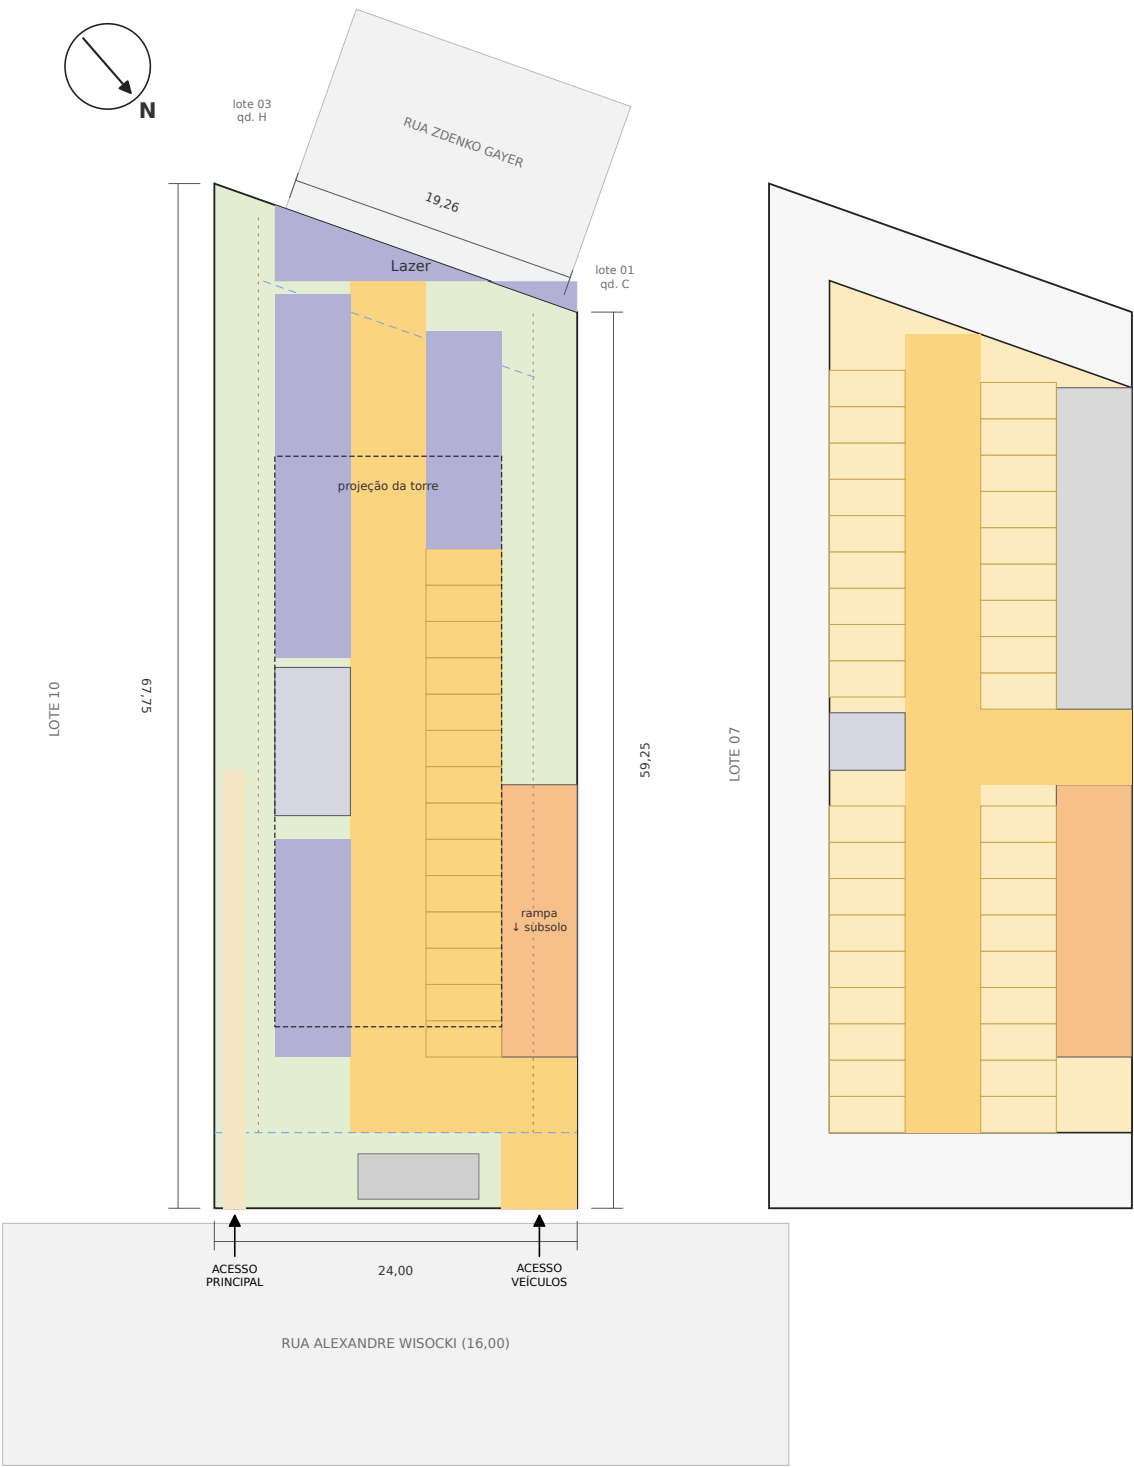

Pavimento Térreo


Subsolo

36 vagas


0 5 10 20
escala 1:500 (m)

- Ap. 2 quartos
- Ap. 3 quartos
- Lazer
- Jardim / área permeável

Linhas tracejadas azuis: recuo frontal de 5,00 m (as duas testadas). Pontilhado vermelho: afastamento H/8 = 2,91 m.

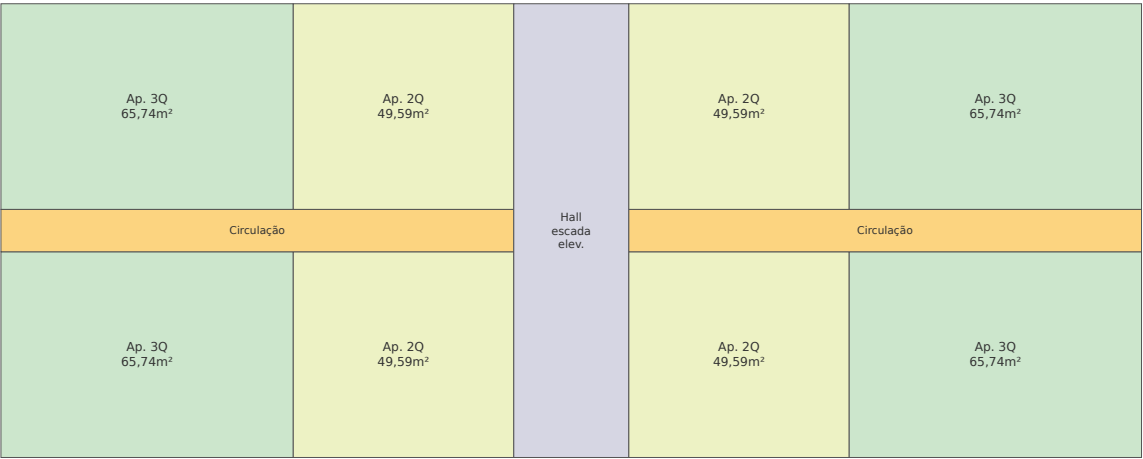

Pavimento Tipo 2Q + 3Q (3x)

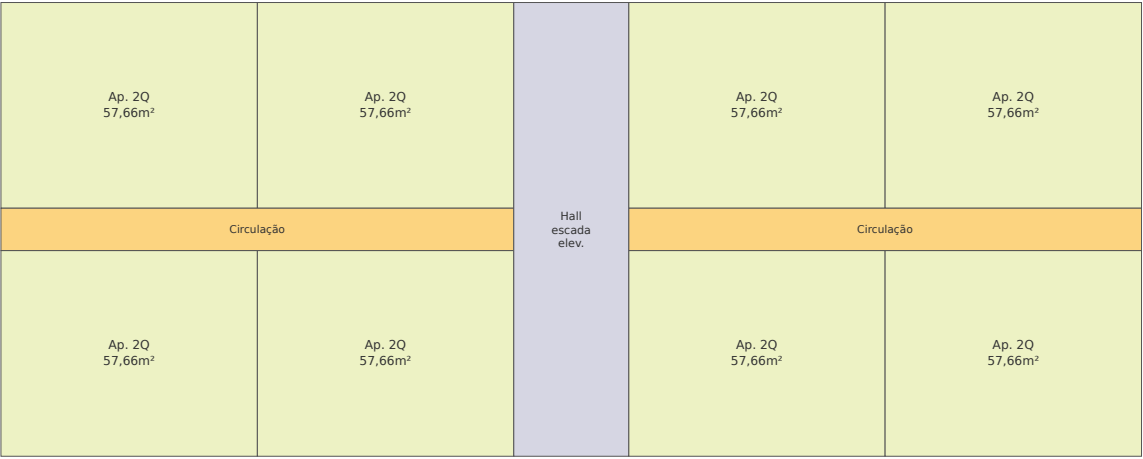

Pavimento Tipo 2Q c/ suite (3x)



Rooftop - ático

Estudo de ocupação

153 • Estudo de Viabilidade

Estudo 1 - 2Q e 3Q, CA básico (2,5) . R00 out.26

PARÂMETROS URBANÍSTICOS

ZR31.524,00m²

R. ALEXANDRE WISOCKI, 249 – Fazenda Velha – Araucária • Paraná • Lote 08-A (Pl. Jardim Orly) • Matrícula 39.537 • Insc. 01.01.00.099.0257 • LC 25/2020, LC 26/2020 e LC 30/2023

Coeficiente Básico	índice	2,50
	área (m²)	3.810,00
Coeficiente Máximo (Compensação Paisagística)	índice	3,00
	área (m²)	4.572,00
Coeficiente Utilizado	índice	2,50
	área (m²)	3.808,98
Tx. de Ocupação – torre	máx.	65%
	utilizada	37,1%
Tx. de Permeabilidade	mín.	20%
	utilizada	25,5%
Altura Padrão / Utilizada (pavimentos)		14 / 7
Afastamento torre (H/8, mín. 2,00) – adotado		2,91 / 4,00 m

Torre única	
Área Privativa Total	2.767,80
Área de Lazer (térreo + rooftop)	958,91
Área Computável Total	3.808,98
Área Construída Total	5.223,03

pavimento	rep.	computável	não comp.	construída	privativa
Subsolo	1x	0,00	1.055,83	1.055,83	0,00
Térreo – pilotis, hall e estacionamento	1x	544,14	21,66	565,80	0,00
Pav. tipo 2Q + 3Q	3x	1.632,42	64,98	1.697,40	1.383,96
Pav. tipo 2Q (c/ suíte)	3x	1.632,42	64,98	1.697,40	1.383,84
Ático – salão de festas/gourmet (≤ 1/3)	1x	0,00	188,60	188,60	0,00
Guarita, lixo e gás (recuo frontal)	1x	0,00	18,00	18,00	0,00
TOTAIS		3.808,98	1.414,05	5.223,03	2.767,80

Área computável conforme LC 26/2020, art. 151 (subsolo de estacionamento, ático ≤ 1/3, escada enclausurada, poço de elevador, guarita, lixo e gás não computáveis).

Resumo Tipologias

Ap. 2 quartos – 49,59 m²	12
Ap. 2 quartos – 57,66 m²	24
Ap. 3 quartos – 65,74 m²	12
TOTAL	48

Vagas de estacionamento

Subsolo S1	36
Térreo (sob pilotis)	14
TOTAL (exigidas: 50)	50
exigência: aptos 1 vaga/un. (48) + studios 1 a cada 3 (0) + visitantes 5% (2) • bicicletas: 7 • capacidade livre no térreo: 22 vagas	

Comparativo das opções (obra • VGV • resultado)

Opção	Unid.	Vagas	Custo obra	VGV	Resultado*	Marg.	EIV
E1 – 2Q e 3Q, CA básico (2,5)	48	50	R\$ 18,2 mi	R\$ 19,2 mi	R\$ 1,0 mi	5%	não
E2 – 2Q e 3Q, CA máximo (3,0)	56	58	R\$ 21,0 mi	R\$ 23,5 mi	R\$ 2,6 mi	11%	não
E3 – 2Q e 3Q, CA máx., 2 subsolos	56	73	R\$ 24,7 mi	R\$ 24,1 mi	R\$ -0,6 mi	-3%	não
E4 – 2Q e studios, CA básico (2,5)	70	44	R\$ 18,4 mi	R\$ 21,5 mi	R\$ 3,1 mi	15%	não
E5 – 2Q e studios, CA máximo (3,0)	96	56	R\$ 21,3 mi	R\$ 26,4 mi	R\$ 5,1 mi	19%	não
E6 – studios + 2Q, CA máximo (3,0)	112	50	R\$ 21,4 mi	R\$ 27,6 mi	R\$ 6,1 mi	22%	não

VGV: 2Q R\$ 7.000/m² • 3Q R\$ 6.800/m² • studio R\$ 8.400/m² • vaga excedente R\$ 35 mil.
Custo: R\$ 3.470/m² construído (torre, térreo, ático) • subsolo R\$ 3.514/m² • +R\$ 5 mil/studio • demolição R\$ 40 mil. CUB-PR ago/2026 (R8-N), ±20%.
*Resultado = VGV – custo da obra – contrapartida EIV. Não inclui terreno, impostos, projetos/aprovação e comercialização.

Verificação legal

CA (LC 25/2020)	2,50 ≤ 2,50	✓
Pavimentos	7 ≤ 14	✓
Afast. torre H/8	4,00 ≥ 2,91 m	✓
TO torre	37,1% ≤ 65%	✓
Vagas (Anexo VII)	50 ≥ 50	✓
Recreação 6 m²/un	959 ≥ 288 m²	✓
Permeabilidade	25,5% ≥ 20%	✓
Studio ≤ 30 m² úteis (art. 258)	—	✓
EIV (Lei 4.688/2025)	não	✓

RESSALVAS

- Lote desenhado a partir da matrícula 39.537 (sem levantamento): laterais tomadas perpendiculares à frente (área 1.524,00 m² confere); fundos calculados 25,46 m x 25,38 m na matrícula.
- Ordem dos segmentos dos fundos (1,20 / 19,18 / 5,00 m) e largura da R. Zdenko Gayer a confirmar; recuo de 5,00 m adotado também nessa testada.
- Cadastro (CND) registra 498,22 m² construídos e a matrícula “sem benfeitorias”: prever demolição e averbação/baixa antes da aprovação.
- CA máximo (3,0) depende da Compensação Paisagística, “a ser regulamentada por lei específica” (LC 25/2020) — confirmar na SMUR.
- Altura máxima subordinada à infraestrutura existente (nota D da ZR3); subsolo a 0 m da divisa com o lote 07 exige contenção — sondagem SPT.
- Preços de venda e custos são premissas do estudo 151 (3Q a R\$ 6.800/m²), não validados em pesquisa de mercado local.



T & L Engenharia

Engenharia e Arquitetura

Araucária • Paraná

Marielen Ferri

Arquitetura e Urbanismo